



РFD · ЛОТ №2 — УЧАСТОК МЕДНОГО И МЕДНО-НИКЕЛЕВОГО КУПОРОСА

синий — раствор/пульпа · оранжевый — греющий пар · фиолетовый — вакуум/соковый пар · зелёный — границы/выходы

НИТКА 1 · МЕДНЫЙ КУПОРОС · 14 139 т/год (1,70 т/ч)

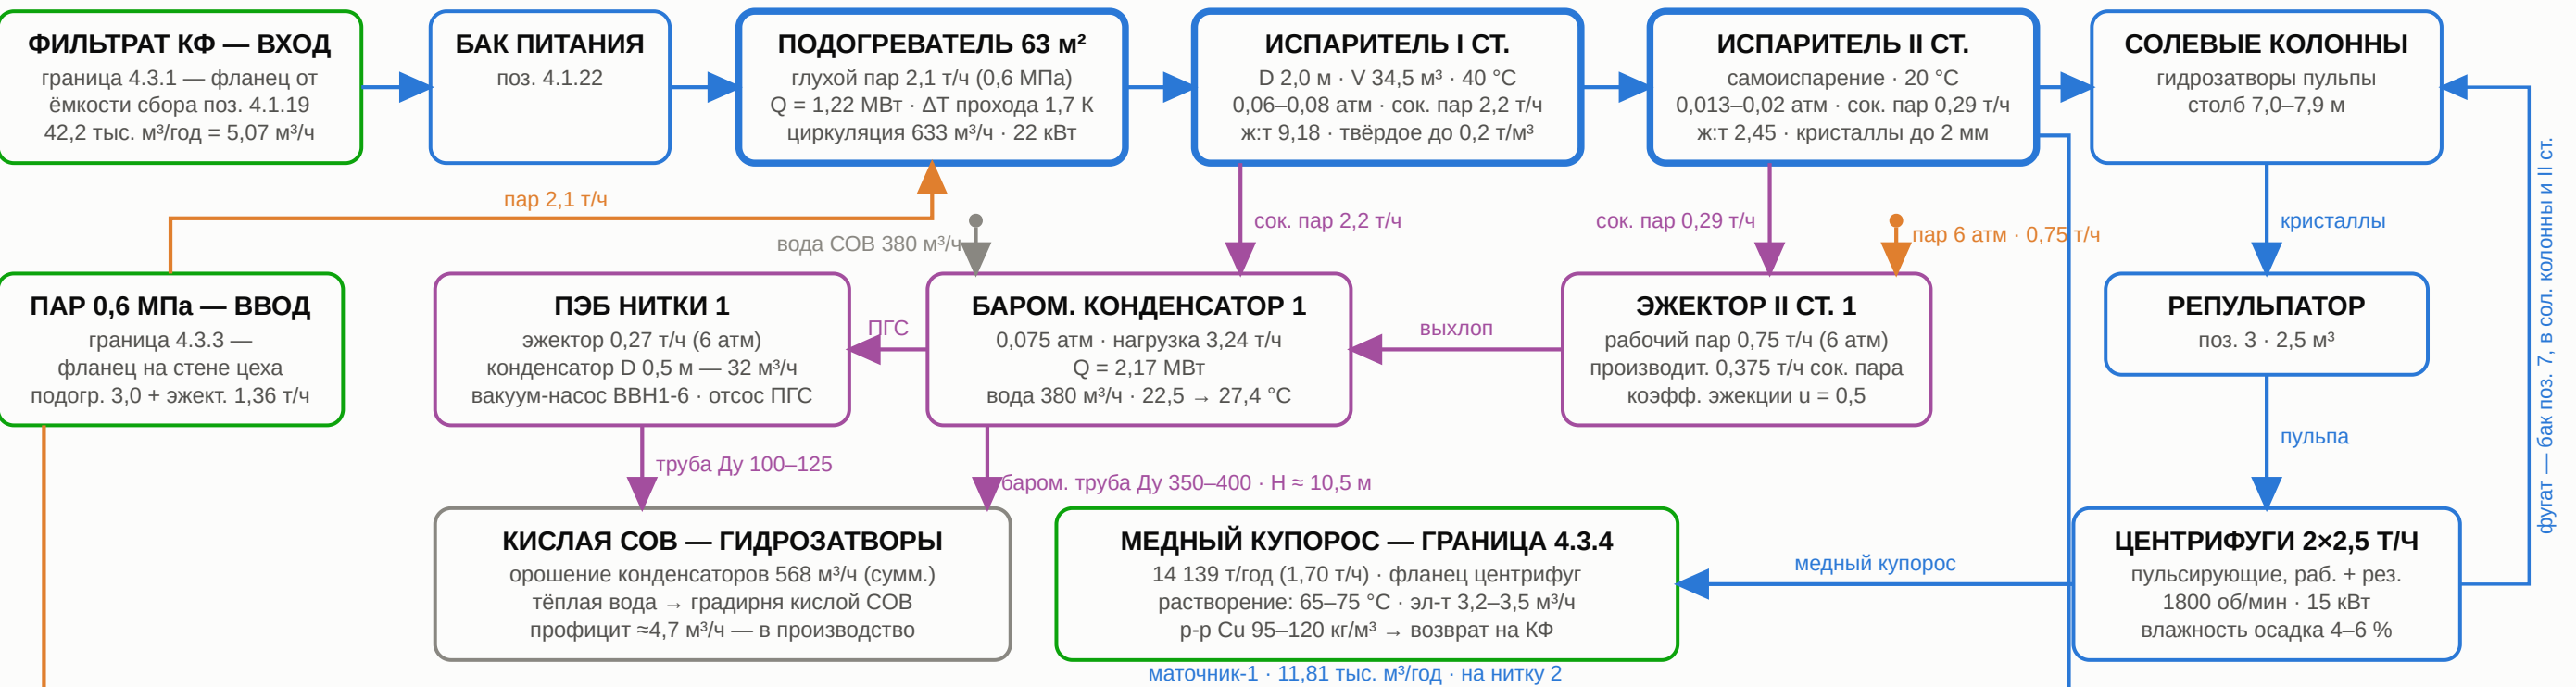

НИТКА 2 · СМЕШАННЫЙ Cu-Ni КУПОРОС · 6 658 т/год (0,80 т/ч)

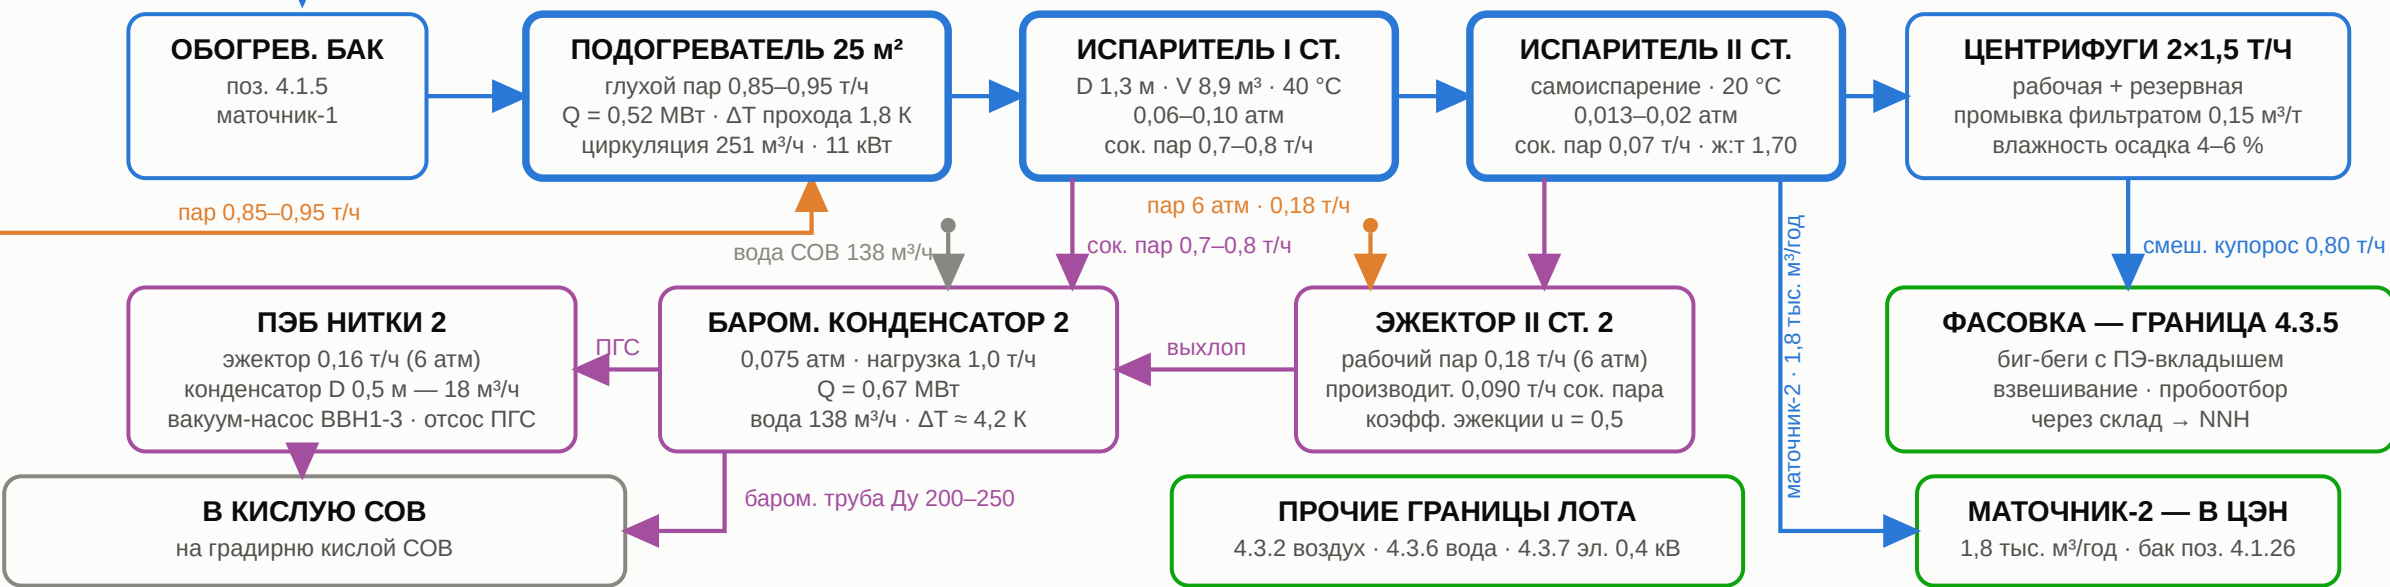

ЭСКИЗ — не для строительства · РFD Лот №2 «Участок купоросов» · жирная обводка = 904L (ИД ч.2 разд. 4.2.1) · источники: база решений БИ — ИД ч.2 табл. 3.1/4.1, рис. 4.4–4.5, расчёт БИ · КВАНТ, черновик БИ

ЭСКИЗНАЯ ПРОРАБОТКА · НЕ ДЛЯ СТРОИТЕЛЬСТВА · РЕВИЗИЯ 0

Изм.	Кол.уч.	Лист	№ док.	Подп.	Дата	ОВЭ75-БИ-Л2-PFD				
0			Р0		02.09.2026					
Разраб.						Комплекс «обжиг – выщелачивание – электроэкстракция» производительностью 75 000 т катодной меди в год КГМК.ОВЭ-75 · Лот №2 «Участок купороса»				
Пров.										
ГИП						Принципиальная технологическая схема		Стадия	Лист	Листов
Н.контр.								БИ · Р0	1	1
Заказчик: АО «Кольская ГМК»						ООО «КВАНТ»				