


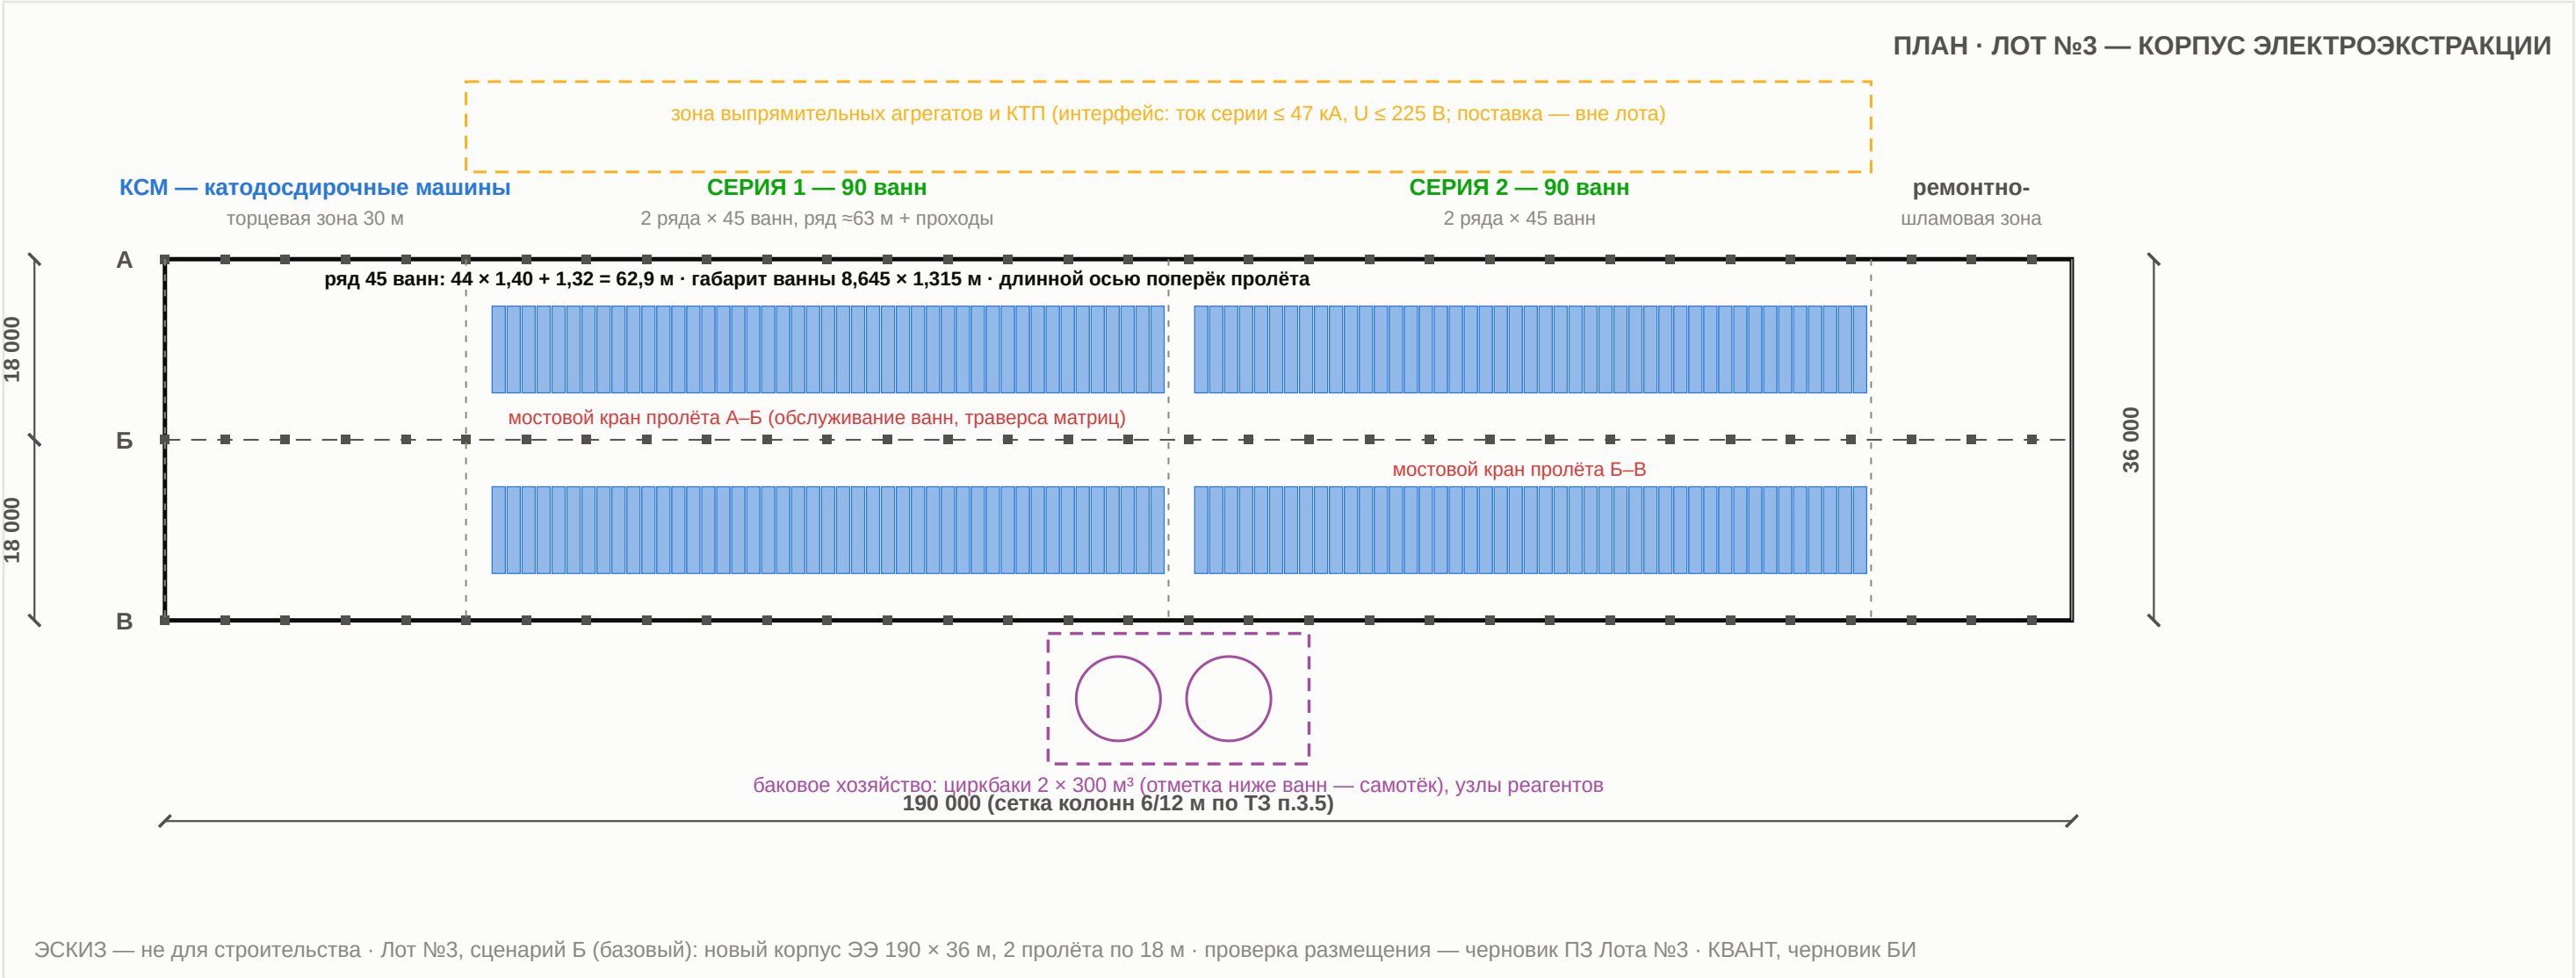


Изм.	Кол.уч.	Лист	№ док.	Подп.	Дата	ОВЭ75-БИ-ЛЗ-КР				
0			Р0		02.09.2026					
Разраб.						Комплекс «обжиг – выщелачивание – электроэкстракция» производительностью 75 000 т катодной меди в год КГМК.ОВЭ-75 · Лот №3 «Отделение электроэкстракции»				
Пров.										
ГИП						План размещения оборудования отделения		Стадия	Лист	Листов
Н.контр.								БИ · Р0	1	2
Заказчик: АО «Кольская ГМК»						ООО «КВАНТ»				

ОВЭ75-БИ-ЛЗ-КР · Разрез по корпусу · Ревизия 0 · 02.09.2026

РАЗРЕЗ · ЛОТ №3 — КОРПУС ЭЛЕКТРОЭКСТРАКЦИИ (СЦЕНАРИЙ Б)

синий — электролит и коллекторы · оранжевый — воздуховод отсоса · фиолетовый — нутч-фильтр · пунктир — предложение БИ / уточняется

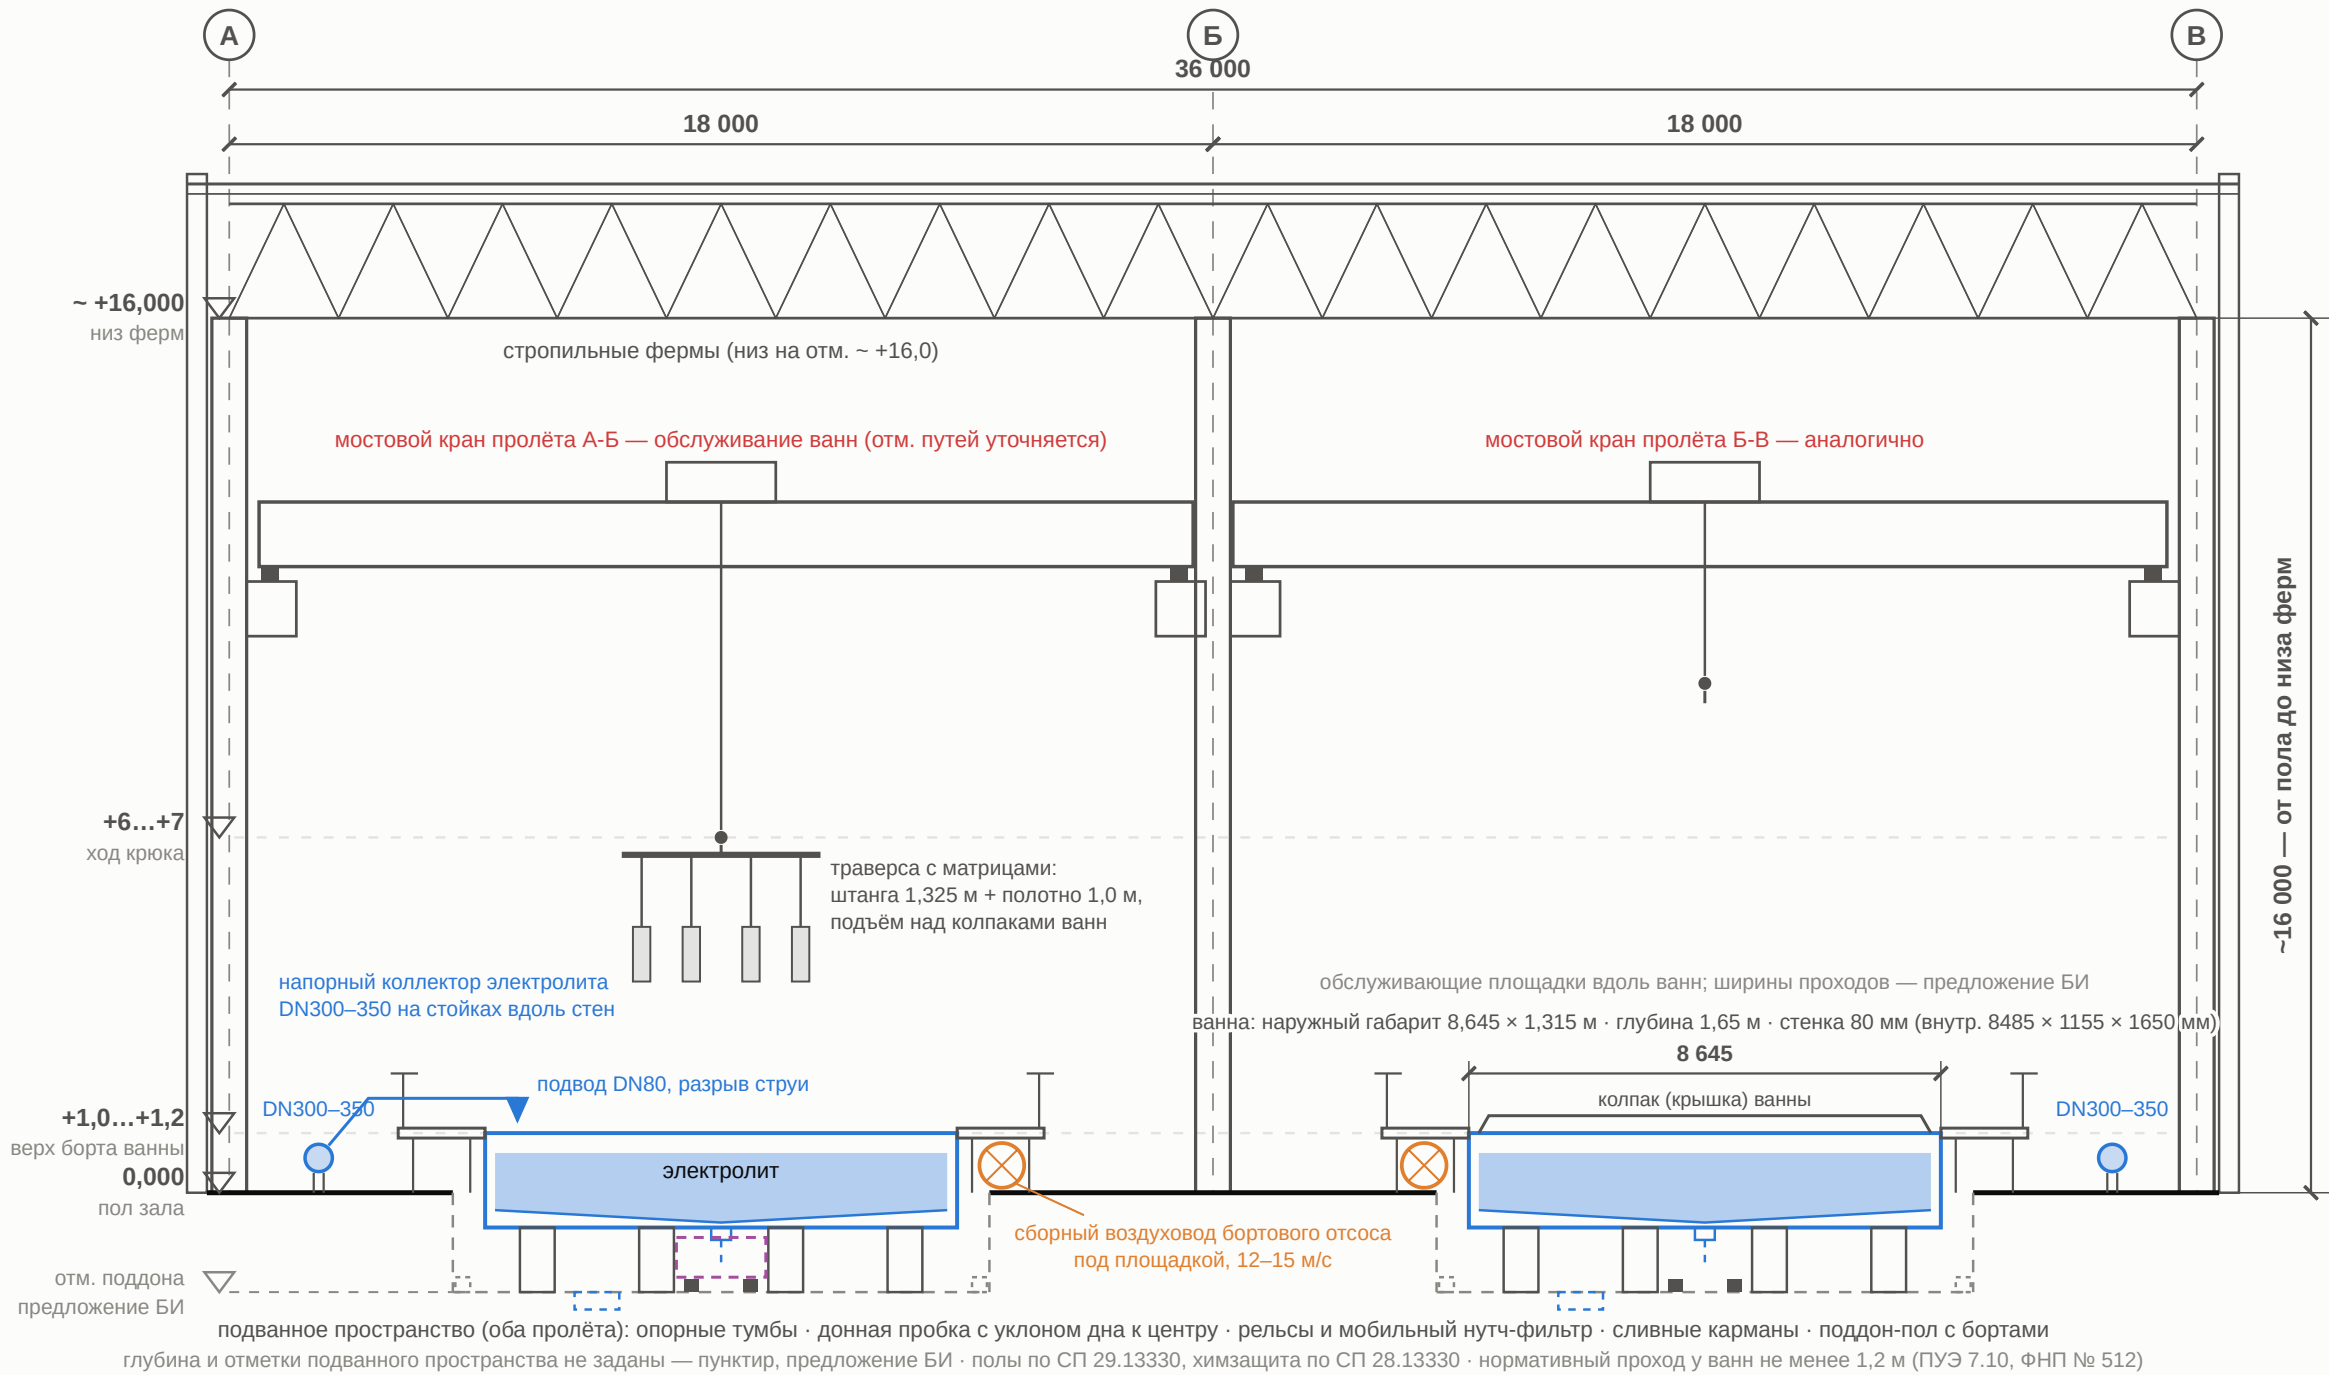

ЭСКИЗ — не для строительства · поперечный разрез корпуса ЭЭ, Лот №3, сценарий Б (36 × 190 м) · источники: черновик ПЗ Лота №3 «Компоновка», ИД ч.2 прил. В · КВАНТ, черновик БИ

Изм.	Кол.уч.	Лист	№ док.	Подп.	Дата	ОВЭ75-БИ-ЛЗ-КР			
0			Р0		02.09.2026				
Разраб.						Комплекс «обжиг – выщелачивание – электроэкстракция» производительностью 75 000 т катодной меди в год КГМК.ОВЭ-75 · Лот №3 «Отделение электроэкстракции»			
Пров.									
ГИП						Разрез по корпусу	Стадия	Лист	Листов
Н.контр.							БИ · Р0	2	2
Заказчик: АО «Кольская ГМК»						ООО «КВАНТ»			