



ЭСКИЗ ОБЩЕГО ВИДА · ЛОТ №1 — ПЕЧЬ КИПЯЩЕГО СЛОЯ (ПОЗ. НО-1)

продольный разрез — схема · размеры в мм, отметки в м · геометрия по ИД ч.1 табл. 23 п.214–217, разд. 2.3
синий — дутьё · оранжевый — газ и огарок · серый — шихта · штриховка — футеровка · пунктир — уточняется по КД

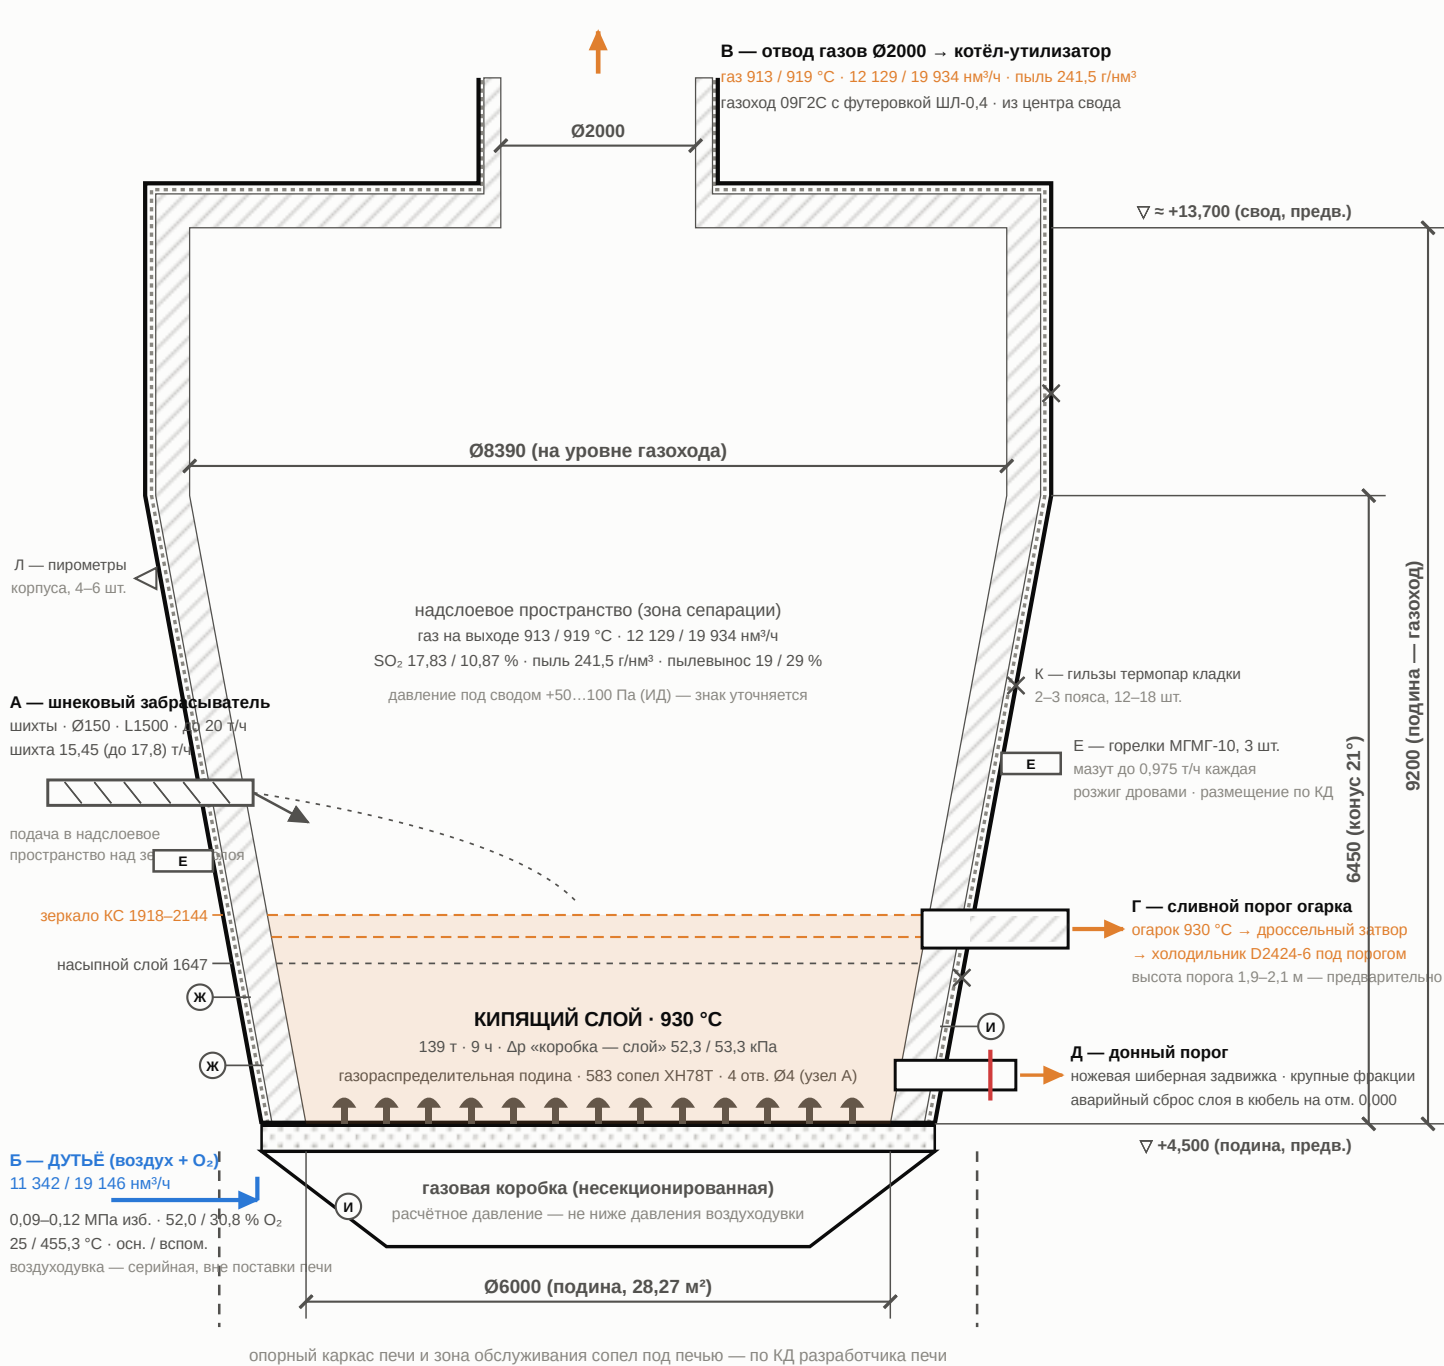

Узел А — сопло подины (схема)


грибовое безпровальное · сталь ХН78Т · 583 шт.
4 отв. Ø4 · шаг и Др решётки — расчёт изготовителя

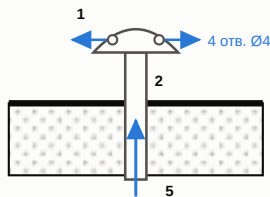

1 — колпак сопла (ХН78Т) · 2 — стойка сопла
3 — плита подины (жаропроч. сталь) · 4 — бетон
5 — газовая коробка · уплотнение сопла — по КД

Схема подины — вид сверху (условно)

Ø6000 · Ø8390 (уровень газохода) · Ø2000

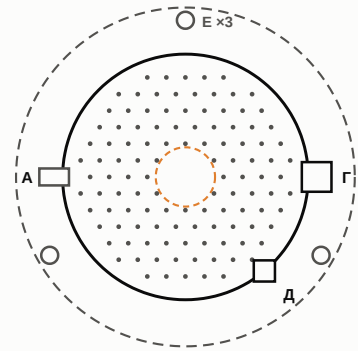

точки — сопла (условно; 583 шт. по КД)
Г — сливной порог · Д — донный порог
А — забрасыватель · Е — горелки (3, через 120°)

Узел Б — стенка корпуса (схема)

снаружи → внутри: корпус (углеродистая сталь),
листовой асбест, шамот Ш-22/23/5/44/45 на мертеле;
рабочее пространство 930 °С



толщины корпуса и футеровки, температурные швы,
перевязка — по проекту футеровки; гильзы термопар
кладки (К) — до кладки, установка после невозможна

Обозн.	Патрубок / закладной элемент	Размер	Кол.
А	Загрузка шихты — забрасыватель	Ø150	1
Б	Подвод дутья в газовую коробку	по КД	1
В	Отвод газов из центра свода	Ø2000	1
Г	Сливной порог, дроссельный затвор	по КД	1
Д	Донный порог, шиберная задвижка	по КД	1
Е	Горелки разогрева МГМГ-10	по КД	3
Ж	Гильзы термопар слоя, 2 уровня	—	8–10
И	Штуцеры давления: слой, коробка	—	2–4
К	Гильзы термопар кладки, 2–3 пояса	—	12–18
Л	Площадки под пирометры корпуса	—	4–6
М	Лючки розжига, люки обслуживания	по КД	по КД

размещение патрубков и закладных элементов — по КД изготовителя

Примечания

- Размеры в мм, отметки в м. Разрез — схема: форма свода, толщины корпуса и футеровки, конструкция опорного каркаса, число и размещение патрубков — по конструкторской документации изготовителя.
- Геометрия рабочего пространства (Ø6000/8390, конус 6450, высота 9200, 583 сопел) — ИД ч.1 табл. 23 п.214–217, разд. 2.3 (конструкция НАТСН); высоты слоя — ИД табл. 23; отметки — компоновка БИ.
- Значения через дробь — основной / вспомогательный вариант дутья по ИД табл. 23.
- Футеровка: листовый асбест, шамот (ориентир 350 мм — оценка, около 135 т); подина — жаропрочная сталь и бетон; сопла — ХН78Т; масса печи с футеровкой 200–230 т (оценка, уточняется по КД).
- Требования к проектированию, изготовлению, контролю и приёмке — документ ОВЭ75-БИ-Л1-НО, поз. НО-1.

ЭСКИЗ — не для строительства · эскиз общего вида печи кипящего слоя, Лот №1, поз. НО-1 · источники: ИД ч.1 табл. 23–25, разд. 2.3–2.4; компоновка БИ Лота №1; расчётная модель КВАНТ

ЭСКИЗНАЯ ПРОРАБОТКА · НЕ ДЛЯ СТРОИТЕЛЬСТВА · РЕВИЗИЯ 0

Изм.	Кол.уч.	Лист	№ док.	Подп.	Дата	ОВЭ75-БИ-Л1-ЭЧ			
0			Р0		02.09.2026				
Разраб.						Комплекс «обжиг – выщелачивание – электроэкстракция» производительностью 75 000 т катодной меди в год КГМК.ОВЭ-75 · Лот №1 «Цех обжига»			
Пров.									
ГИП						Печь кипящего слоя — эскиз общего вида	Стадия	Лист	Листов
Н.контр.							БИ · Р0	1	1
Заказчик: АО «Кольская ГМК»						ООО «КВАНТ»			