


ВЫСОТНАЯ СХЕМА · ЛОТ №1 — ГЛАВНЫЙ КОРПУС ЦЕХА ОБЖИГА
продольный технологический разрез-схема (развёртка по цепочке аппаратов) · отметки в метрах

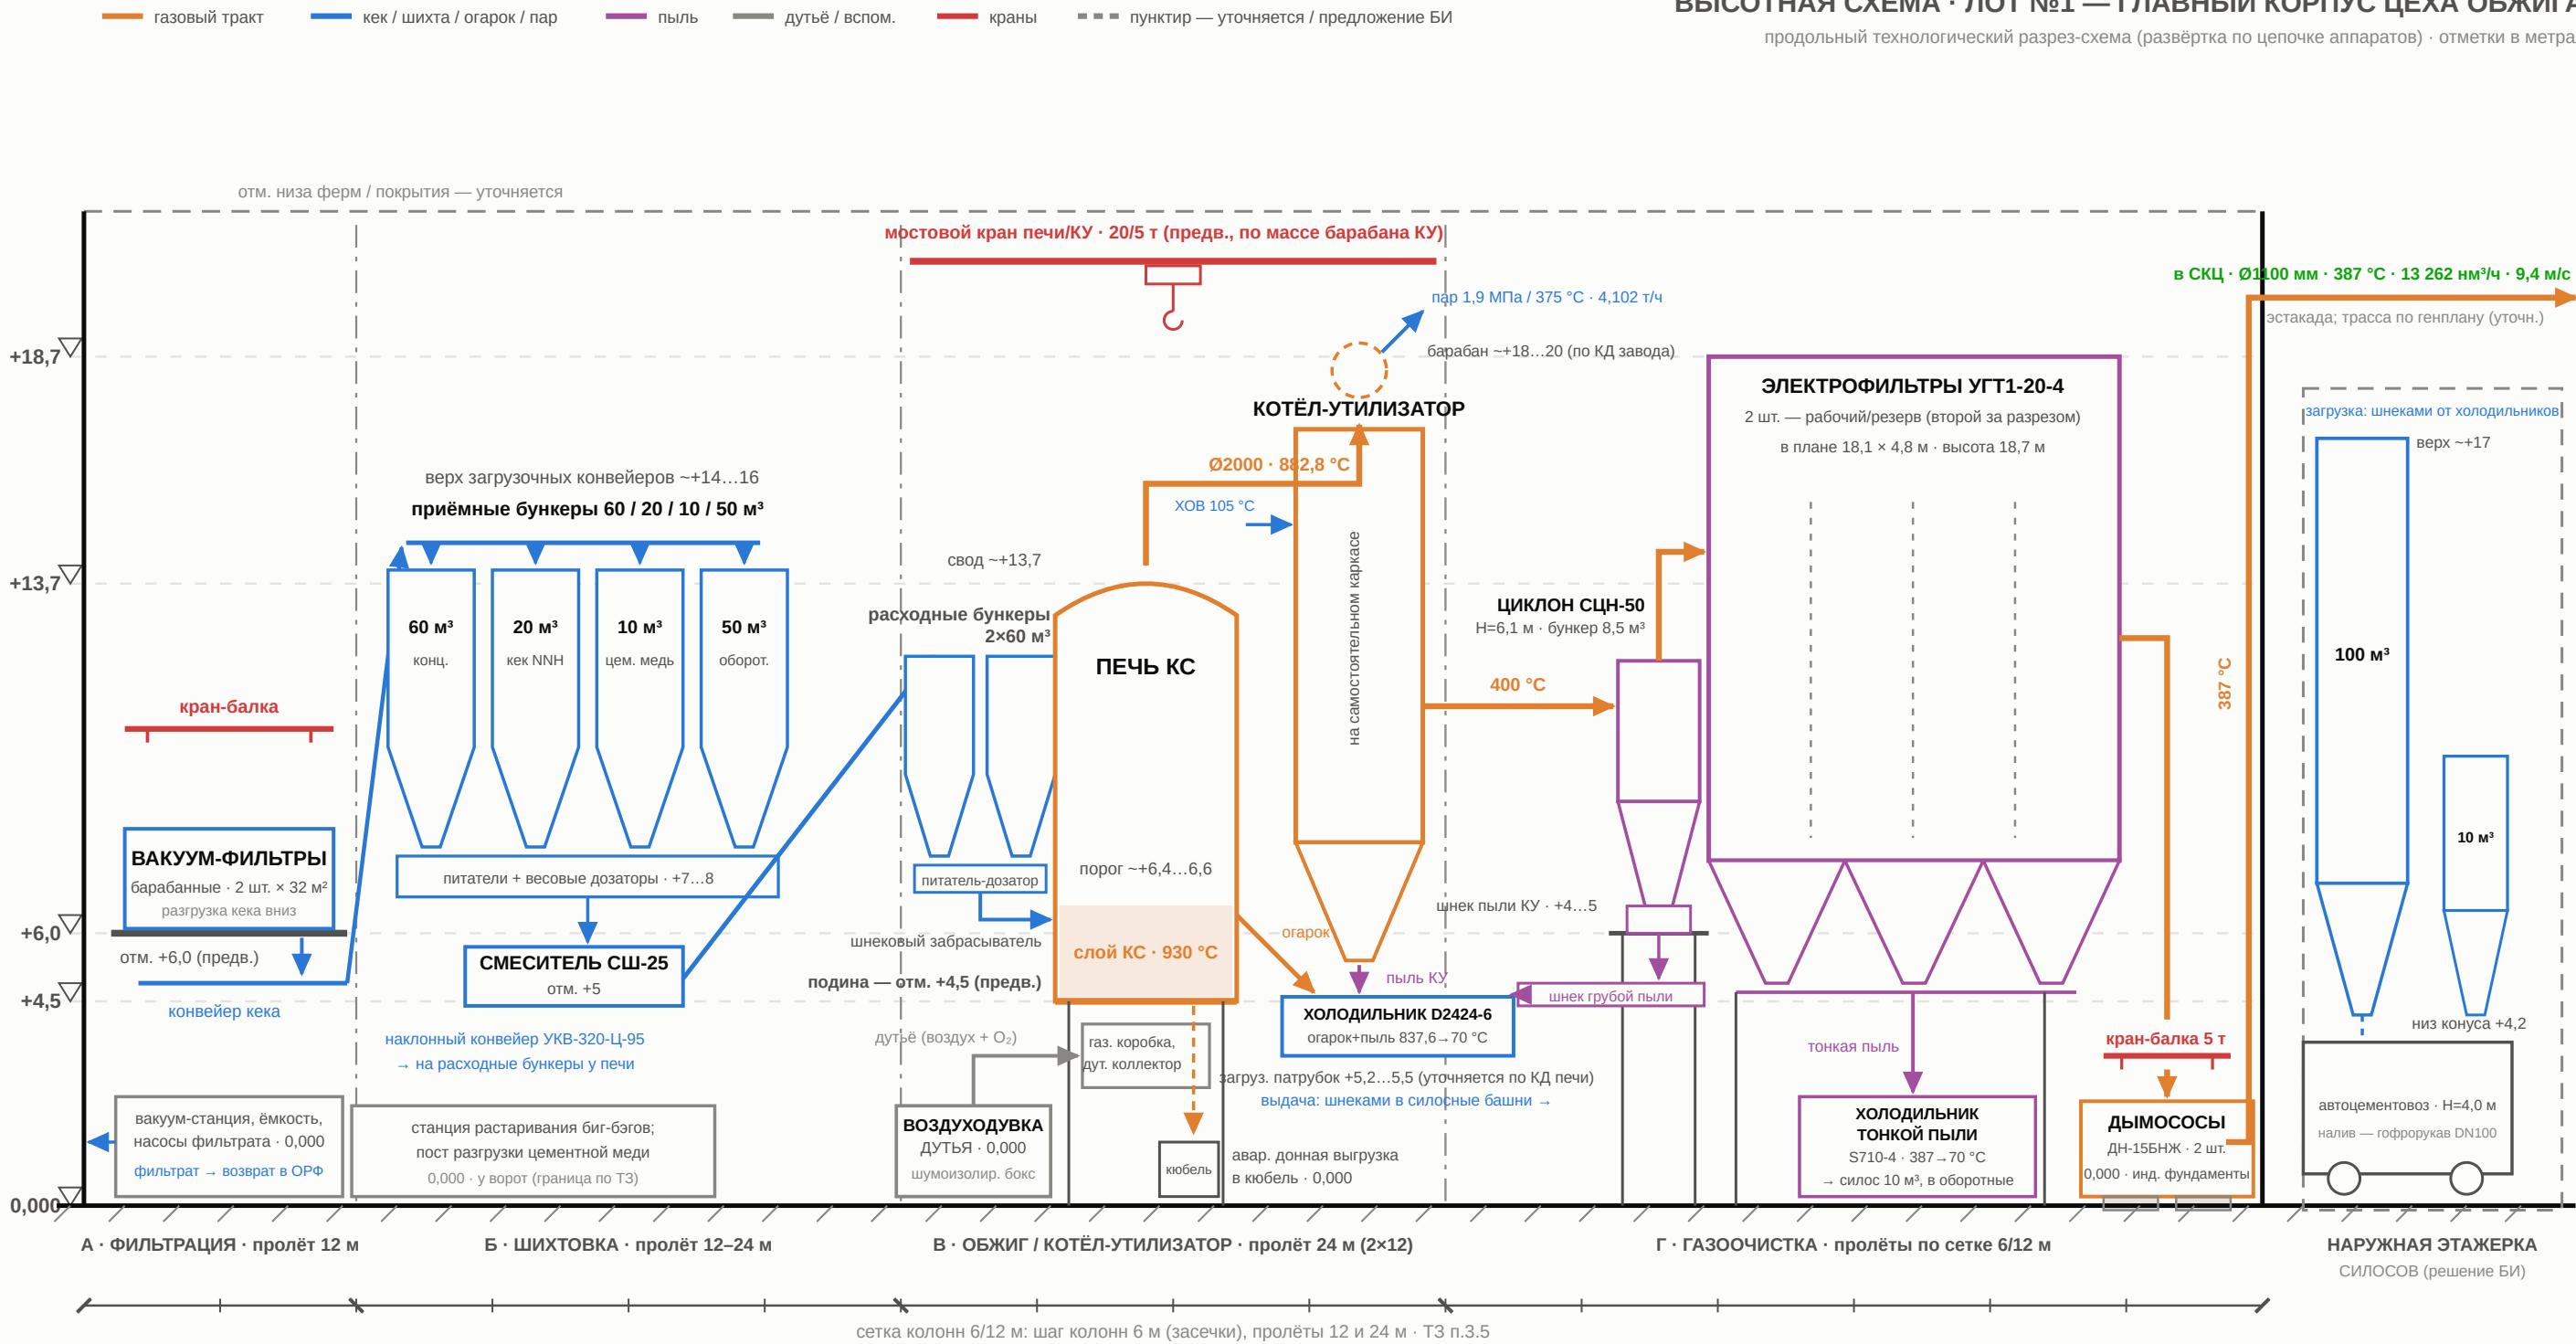

ЭСКИЗ — не для строительства · высотная схема гл. корпуса цеха обжига (Лот №1), разрез-развёртка · источники: БИ Лот №1 — компоновка, теплобалансы, PFD (ИД табл. 23; ТЗ п.3.5) · КВАНТ, черновик БИ

Изм.	Кол.уч.	Лист	№ док.	Подп.	Дата	ОВЭ75-БИ-Л1-КР			
0			Р0		02.09.2026				
Разраб.						Комплекс «обжиг – выщелачивание – электроэкстракция» производительностью 75 000 т катодной меди в год КГМК.ОВЭ-75 · Лот №1 «Цех обжига»			
Пров.									
ГИП						Высотная схема размещения оборудования	Стадия	Лист	Листов
Н.контр.							БИ · Р0	1	1
Заказчик: АО «Кольская ГМК»						ООО «КВАНТ»			

ЭСКИЗНАЯ ПРОРАБОТКА · НЕ ДЛЯ СТРОИТЕЛЬСТВА · РЕВИЗИЯ 0