



75 000 т/год · приёмка 209,5 т/сут = 84 пакета/сут (по 2,5 т) · пик 7 пак./ч · буфер 1200 пакетов = 3000 т ≈ 14,3 сут · площадь СГП ≈2500–3000 м²

ПЛАН · ЛОТ №4 — СКЛАД ГОТОВОЙ ПРОДУКЦИИ

эскиз компоновки · приёмка → адресное хранение → фронты отгрузки

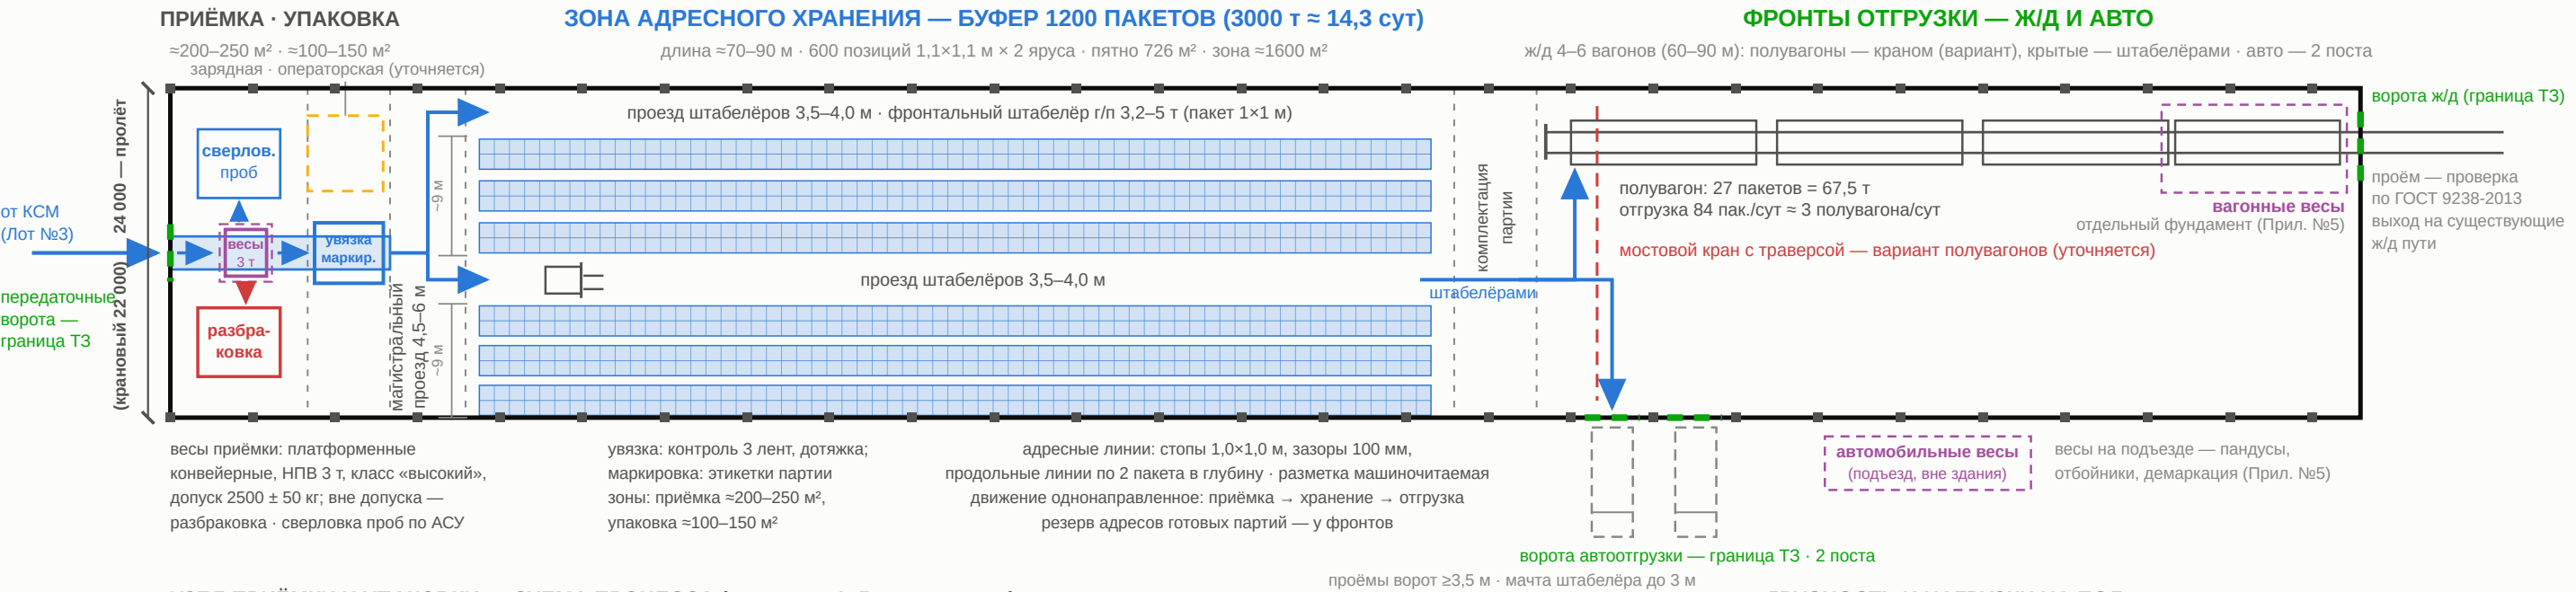

УЗЕЛ ПРИЁМКИ И УПАКОВКИ — СХЕМА ПРОЦЕССА (операции 1–5 техпроцесса)

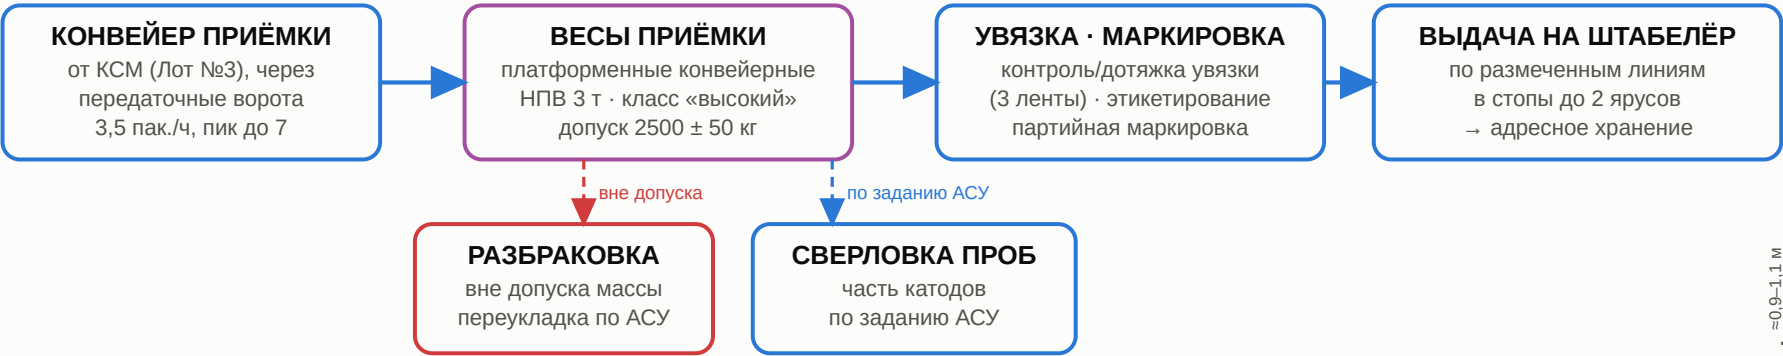

Поток: 75 000 т/год = 209,5 т/сут (358 сут) · буфер покрывает: партия-маршрут 1350 т (20 полувагонов × 27 пакетов) в наборе + готовая партия в ожидании подачи + страховой запас 2–3 сут + технологический запас (химанализ) 1–2 сут · минимум 1500 т (7 сут)

Базис размещения — ТЗ v4.1 п. 1.3 (новый склад ГП, задание на новый корпус); показана компоновка в пролёте 24 м с шагом колонн 6 м по разд. «Компоновочные решения» (резервный сценарий А — ЦЭМ); зонирование нового корпуса аналогично.
Цвета: синий — поток продукции и адресные линии · фиолетовый — весовые зоны · зелёный пунктир — границы проектирования по ТЗ (ворота) · красный — разбраковка, кран (вариант) · жёлтый — зарядная · пунктиром — предложения БИ (уточняется).

ЭСКИЗ — не для строительства · Лот №4: план склада готовой продукции (пролёт 24 м, сценарий А) · источники: база решений БИ («Компоновка», «Ёмкость», «Полы», техпроцесс) · КВАНТ, черновик БИ

ЭСКИЗНАЯ ПРОРАБОТКА · НЕ ДЛЯ СТРОИТЕЛЬСТВА · РЕВИЗИЯ 0

Изм.	Кол.уч.	Лист	№ док.	Подп.	Дата	ОВЭ75-БИ-Л4-КР			
0			Р0		02.09.2026				
Разраб.						Комплекс «обжиг – выщелачивание – электроэкстракция» производительностью 75 000 т катодной меди в год КГМК.ОВЭ-75 · Лот №4 «Склад готовой продукции»			
Пров.									
ГИП						План склада готовой продукции	Стадия	Лист	Листов
Н.контр.							БИ · Р0	1	1
Заказчик: АО «Кольская ГМК»						ООО «КВАНТ»			