


РFD · ЛОТ №3 — ОТДЕЛЕНИЕ ЭЛЕКТРОЭКСТРАКЦИИ

синий — растворы и электролит · жёлтый — постоянный ток и ошиновка · зелёный — товарный продукт и границы лота · фиолетовый — аспирация · серый — вспомогательные потоки
пунктирная обводка блока — оборудование вне поставки Лота №3 (БИ выдаёт задание на стыке) · мелким шрифтом под блоком — источник чисел

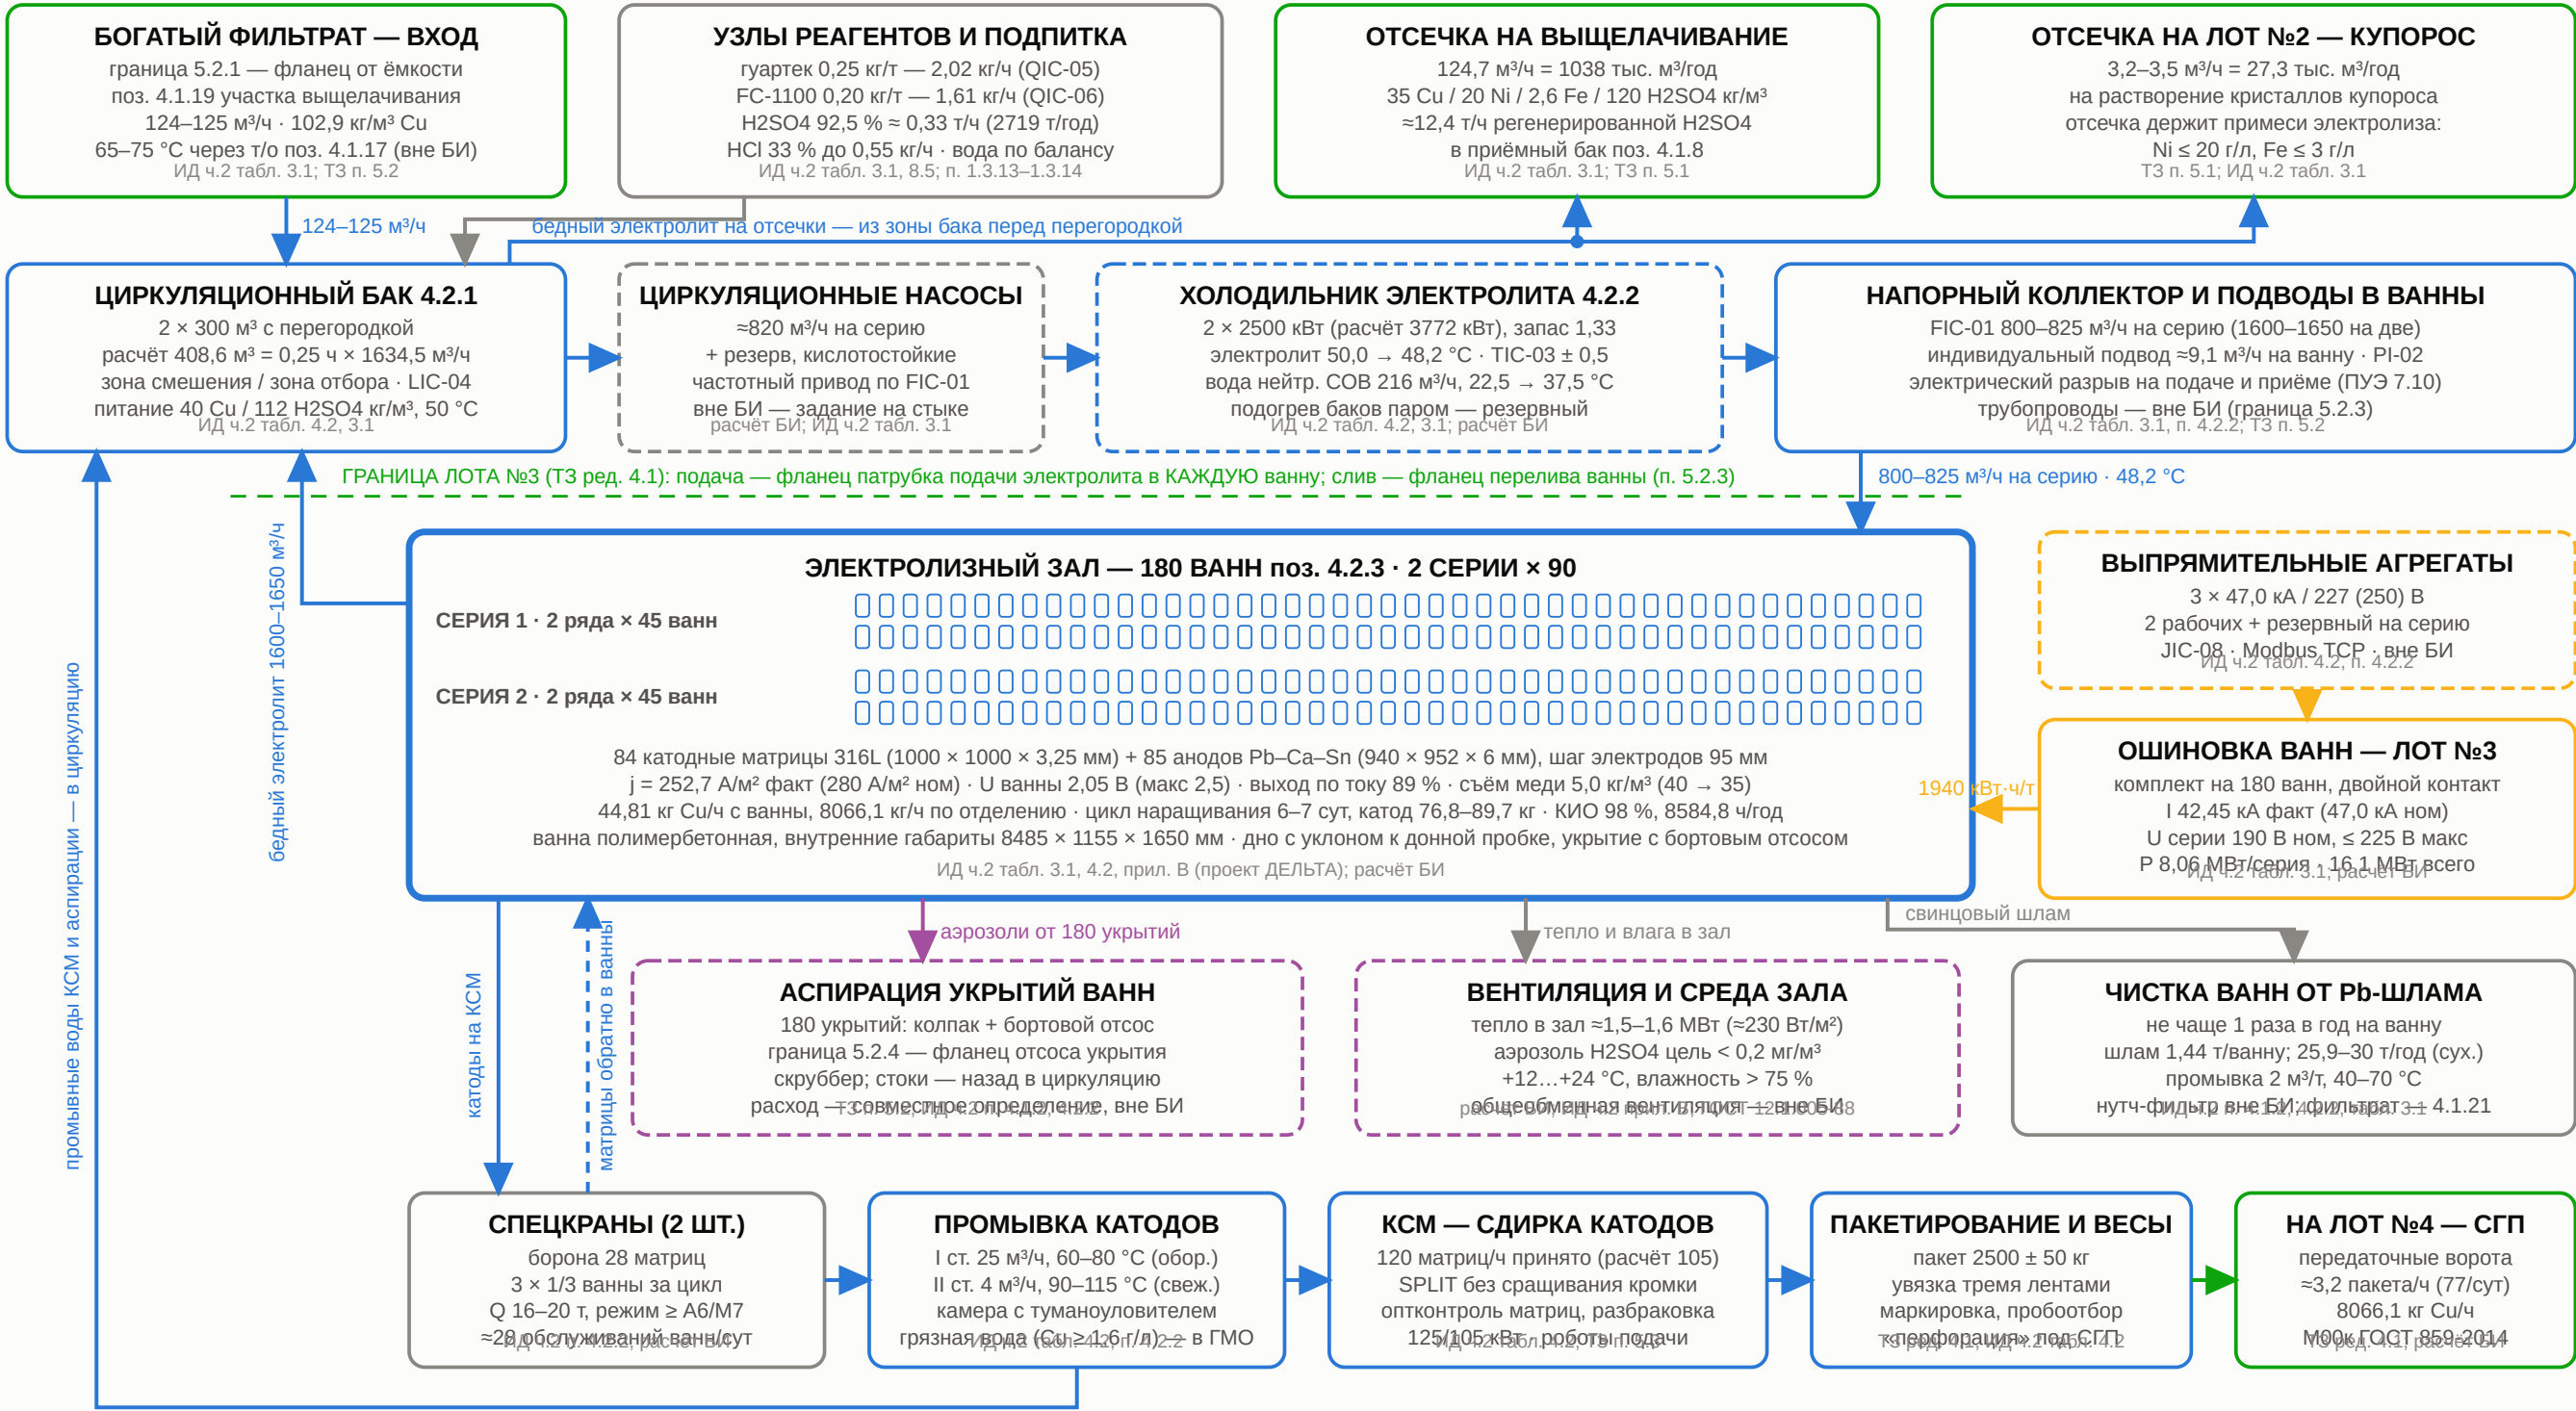

ЭСКИЗ — не для строительства · PFD Лот №3 «Отделение электроэкстракции» · источники: ИД ч.2 табл. 3.1, 4.2, 8.5, прил. В (проект ДЕЛЬТА), ТЗ ред. 4.1 п. 5.1–5.3, расчёт БИ · КВАНТ, черновик БИ

ЭСКИЗНАЯ ПРОРАБОТКА · НЕ ДЛЯ СТРОИТЕЛЬСТВА · РЕВИЗИЯ 0

Изм.	Кол.уч.	Лист	№ док.	Подп.	Дата	ОВЭ75-БИ-ЛЗ-PFD			
0			Р0		02.09.2026				
Разраб.						Комплекс «обжиг – выщелачивание – электроэкстракция» производительностью 75 000 т катодной меди в год КГМК.ОВЭ-75 · Лот №3 «Отделение электроэкстракции»			
Пров.									
ГИП						Принципиальная технологическая схема	Стадия	Лист	Листов
Н.контр.							БИ · Р0	1	1
Заказчик: АО «Кольская ГМК»						ООО «КВАНТ»			